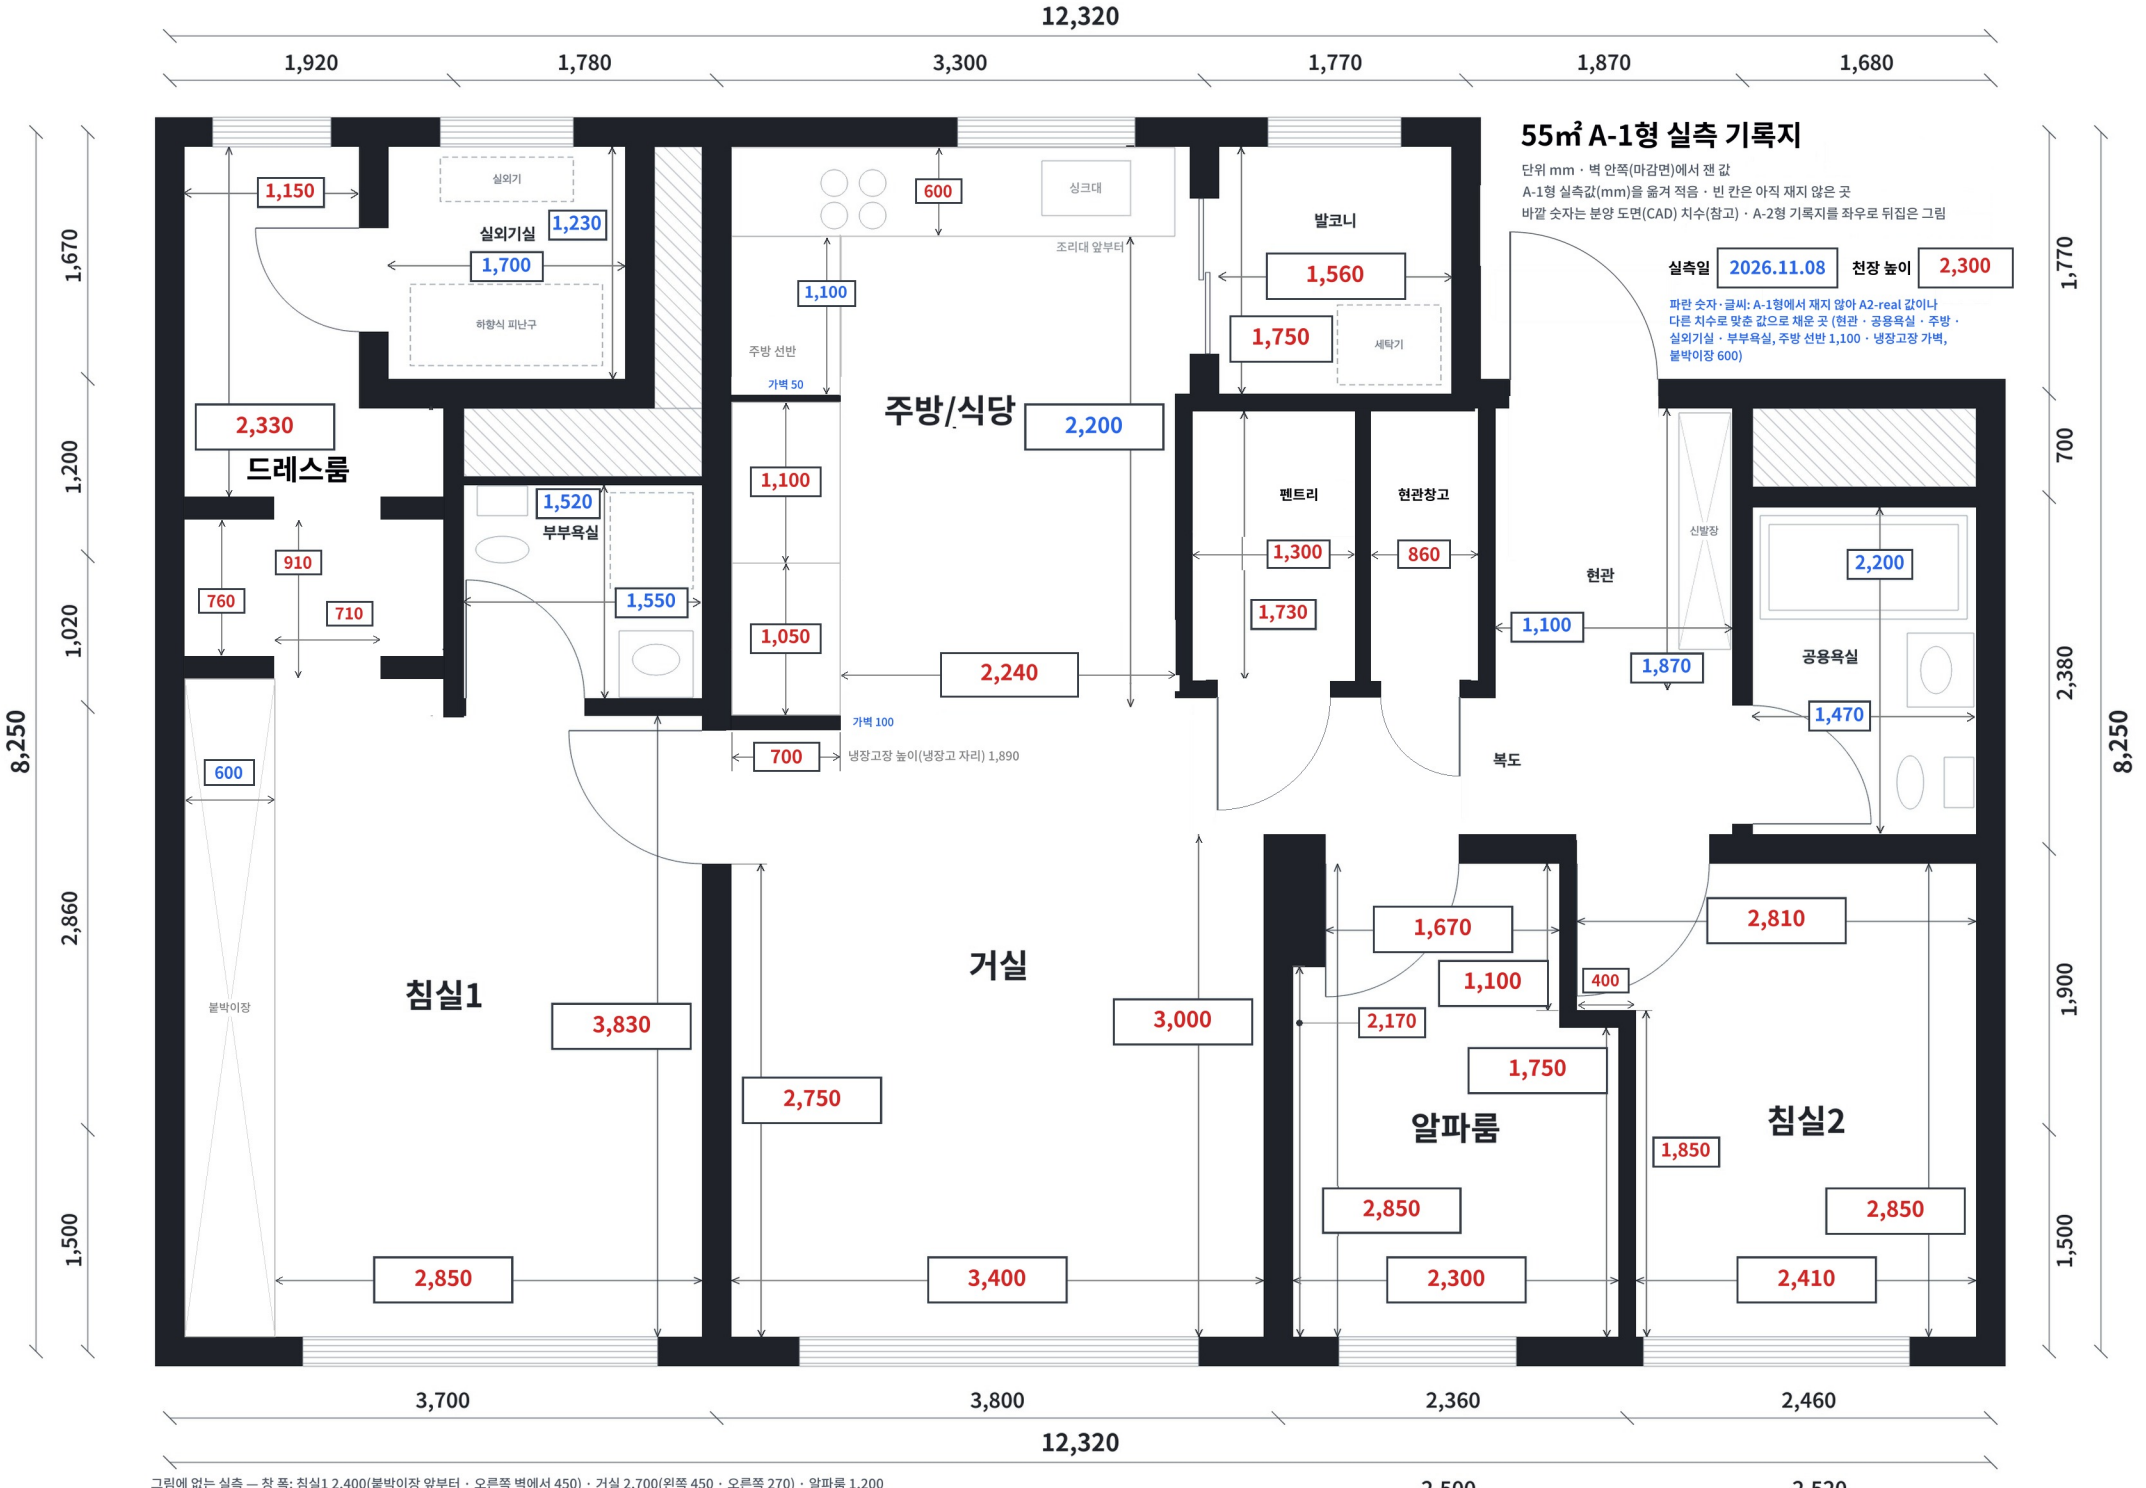


그림에 없는 실측 — 창 폭: 침실1 2,400(붙박이장 앞부터 · 오른쪽 벽에서 450) · 거실 2,700(왼쪽 450 · 오른쪽 270) · 알파룸 1,200 · 침실2 1,800(오른쪽 벽에서 460) · 드레스룸 800 · 발코니 900 / 창 높이: 거실·침실1 2,300 · 드레스룸 1,300 · 발코니 1,160
창 아래(바닥부터): 침실2 1,220 · 알파룸 1,200 / 현관문은 밖으로 열림 / 발코니 위 1,450 · 왼쪽 1,500 · 세탁기 바닥 1,600 × 900 · 알파룸 문 옆 770 · 침실2 문 옆 1,800 · 침실1 문 아래 2,800

분양 안내 사진 치수 (바깥 벽면 기준) →