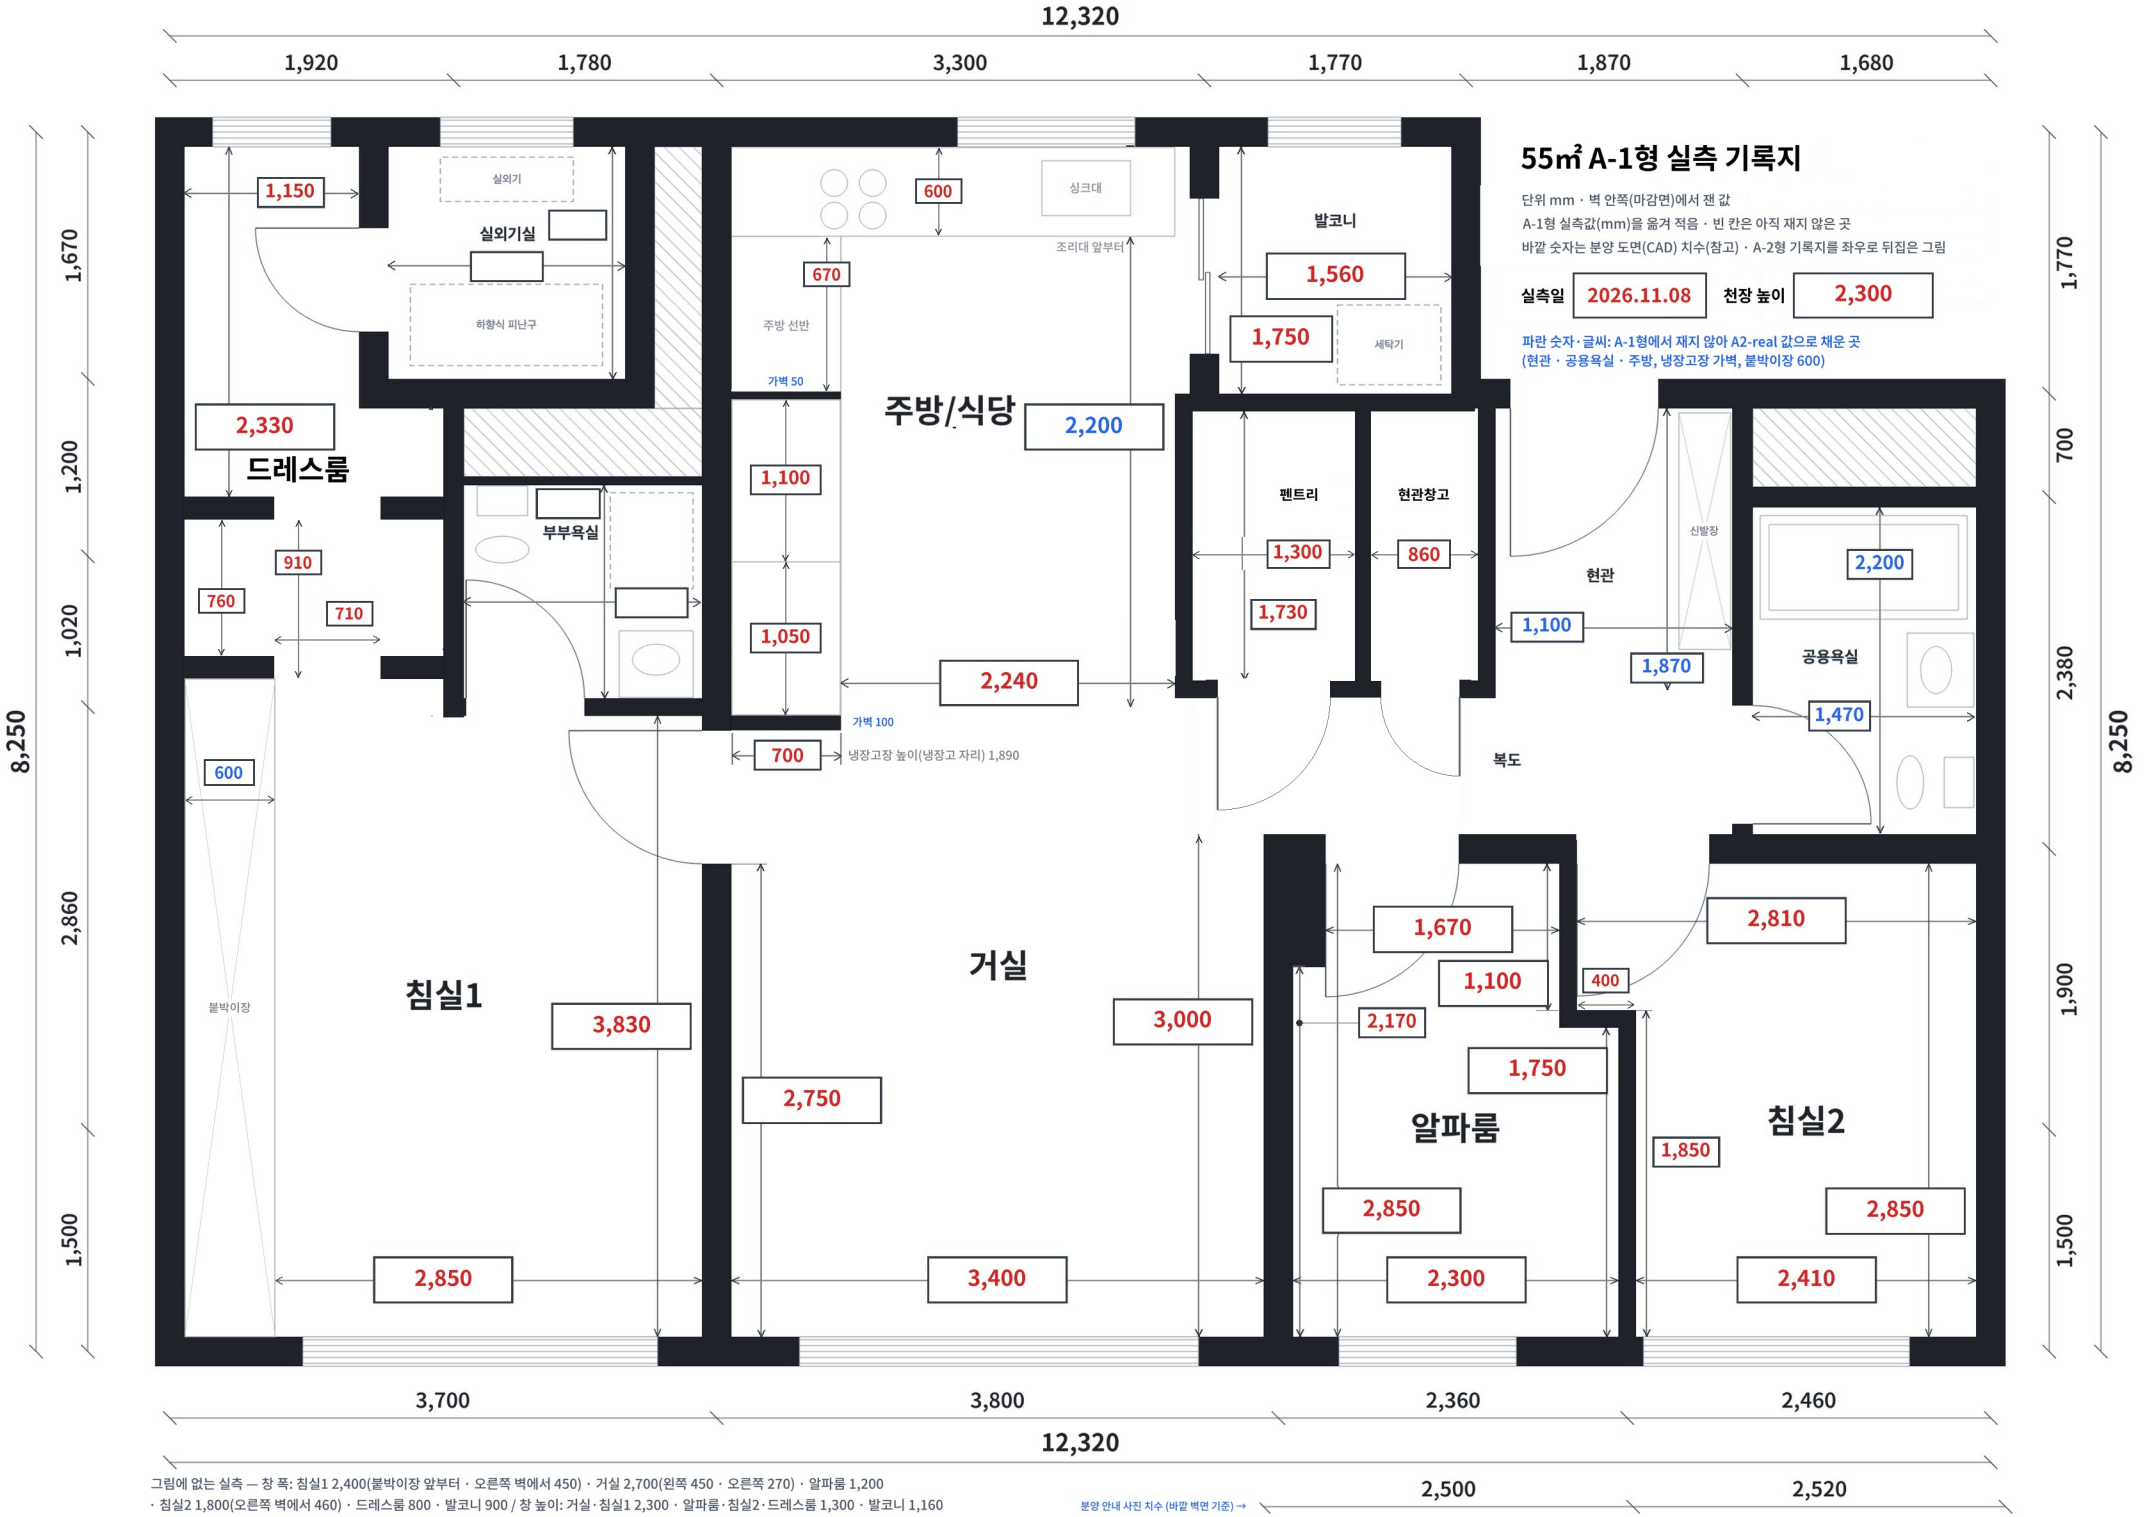

12,320
1,920
1,780
3,300
1,770
1,870
1,680
8,250
1,670
1,200
1,020
2,860
1,500
55㎡ A-1형 실측 기록지
단위 mm · 벽 안쪽(마감면)에서 잰 값
A-1형 실측값(mm)을 옮겨 적음 · 빈 칸은 아직 재지 않은 곳
바깥 숫자는 분양 도면(CAD) 치수(참고) · A-2형 기록지를 좌우로 뒤집은 그림
실측일 2026.11.08
천장 높이 2,300
파란 숫자·글씨: A-1형에서 재지 않아 A2-real 값으로 채운 곳
(현관 · 공용욕실 · 주방, 냉장고장 가벽, 붙박이장 600)
드레스룸
2,330
1,150
910
760
710
600
붙박이장
실외기
실외기실
하향식 피난구
부부욕실
주방/식당
2,200
600
싱크대
조리대 앞부터
670
주방 선반
가벽 50
1,100
1,050
2,240
가벽 100
700
냉장고장 높이(냉장고 자리) 1,890
발코니
1,560
1,750
세탁기
펜트리
현관창고
1,300
860
1,730
현관
1,100
1,870
신발장
2,200
공용욕실
1,470
복도
침실1
3,830
2,750
2,850
거실
3,000
3,400
1,670
1,100
400
2,170
1,750
알파룸
1,850
2,850
2,300
침실2
2,810
2,850
2,410
1,770
700
2,380
1,900
1,500
8,250
3,700
3,800
2,360
2,460
12,320
2,500
2,520
그림에 없는 실측 — 창 폭: 침실1 2,400(붙박이장 앞부터 · 오른쪽 벽에서 450) · 거실 2,700(왼쪽 450 · 오른쪽 270) · 알파룸 1,200
· 침실2 1,800(오른쪽 벽에서 460) · 드레스룸 800 · 발코니 900 / 창 높이: 거실·침실1 2,300 · 알파룸·침실2·드레스룸 1,300 · 발코니 1,160
발코니 위 1,450 · 왼쪽 1,500 · 세탁기 바닥 1,600 × 900 · 알파룸 문 옆 770 · 침실2 문 옆 1,800 · 침실1 문 아래(침실1 쪽) 2,800
분양 안내 사진 치수 (바깥 벽면 기준) →