
55㎡ B-2형 실측 기록지

단위 mm · 벽 안쪽(마감면)에서 잰 값
현장 실측 사진(손글씨, cm)의 값을 mm로 옮겨 적음
바깥 숫자는 B2-real 도면 치수(참고)

실측일 —

천장 높이 2,300

자료 출처 5205동IT*

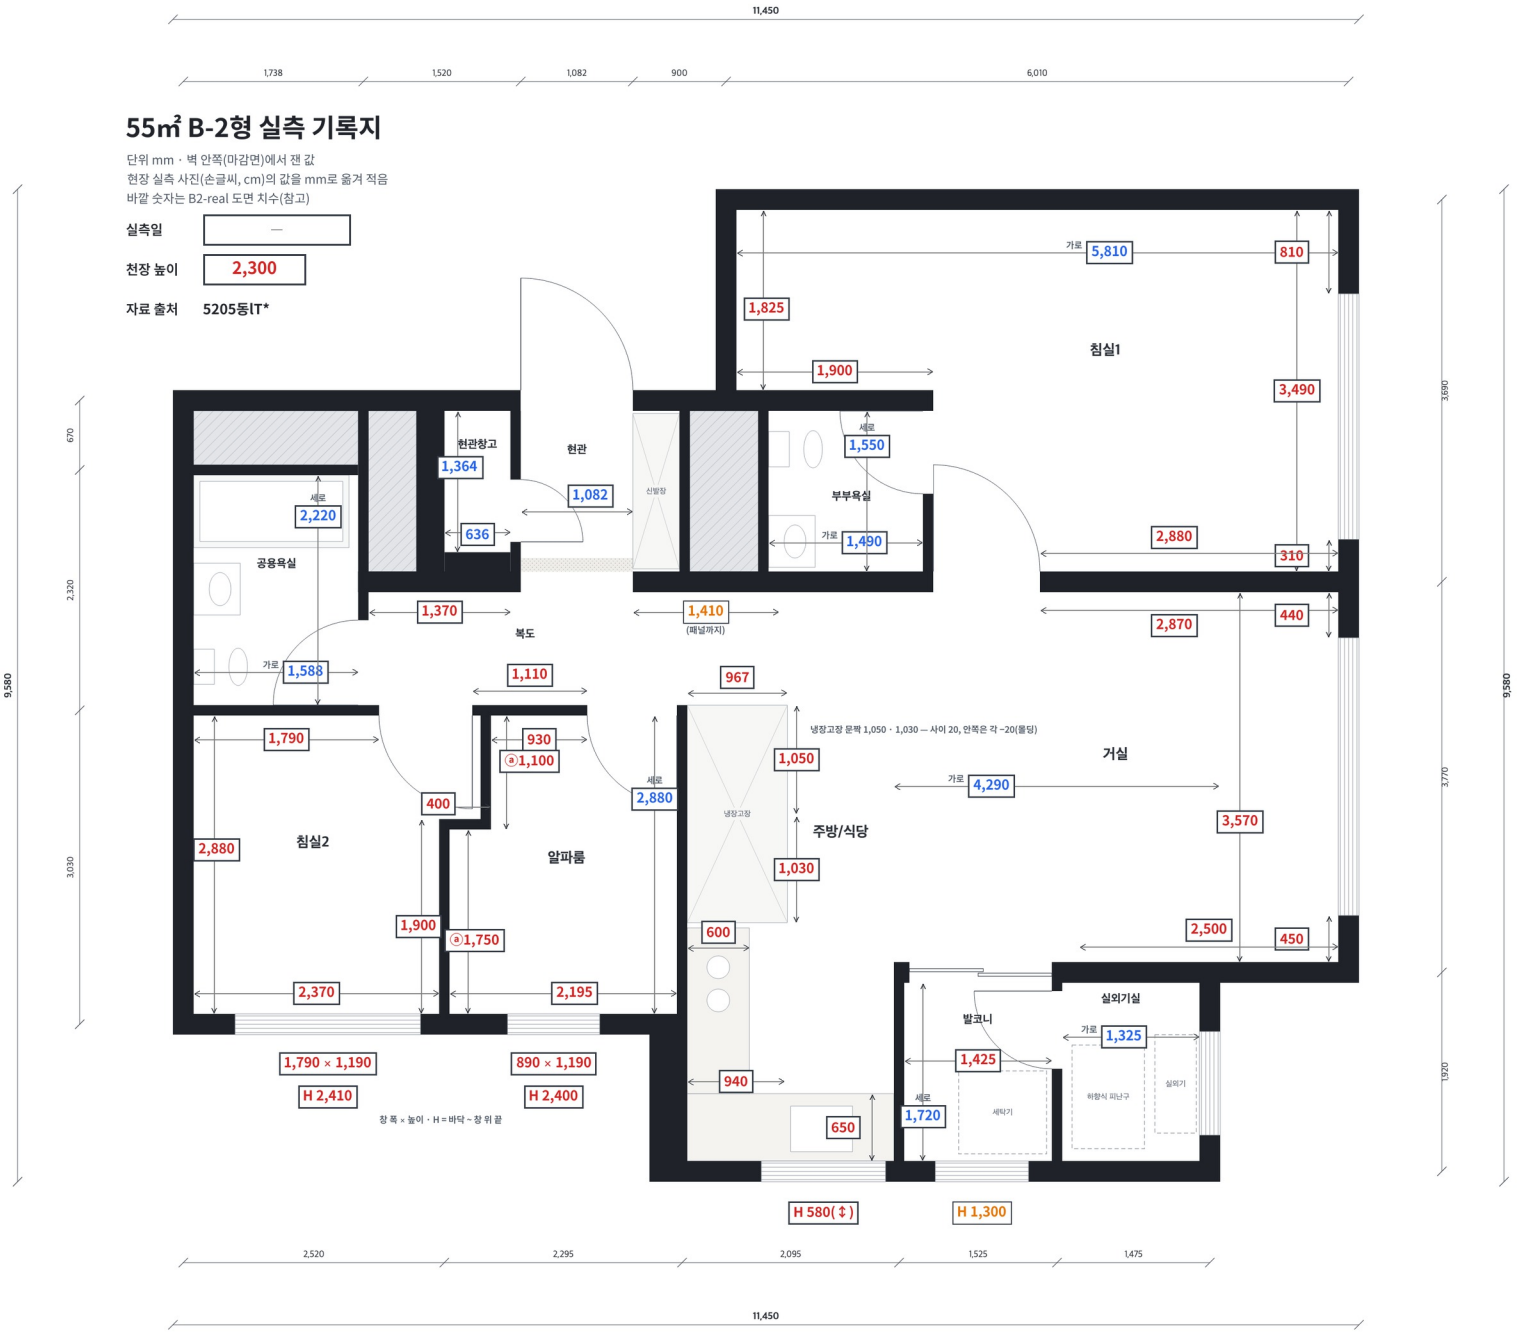

읽는 법

- **1,234** 사진에서 읽은 값 (cm → mm)
- **1,234** 사진에 적혔지만 어디를 잰 것인지 확인이 필요한 값
- **1,234** 안 잰 곳 — B1-real 값(같은 모양, B2 실측 아님)
- **ⓐ1,100** 나눠 잰 값의 합이 전체와 다름 — 같은 글자끼리

확인이 필요한 글씨

- ⓐ 알파룸 쪽 칸막이 1,100 + 꺾인 벽 100 + 1,750 = 2,950
  — 침실2 세로 2,880과 70 차이. 도면은 아래쪽을 1,780으로 맞춤
- 침실1 오른쪽 349 — 창 길이가 아니라 침실1 세로로 봄
  — 81 + 349 + 31 = 4,610은 너무 김. 창은 3,490 − 810 − 310 = 2,370
- 침실1 드레스 자리 세로 1,825
  — 세로 3,490 · 부부욕실과 맞지 않아 도면은 1,740
- 복도 위 141(패널까지) — 현관 오른쪽부터 어디까지인지 확인
- 냉장고장 96.7 — 벽 ~ 앞면 깊이 967로 봄 (그림보다 깊음)
- 주방 인덕션 줄 쪽 60 두 개 · 76 — 하나는 줄 깊이 600으로 봄
  — 나머지 60 · 76은 어디를 잰 것인지 확인
- 창 H241 · H240 — 바닥 ~ 창 위 끝으로 봄 (창 아래 1,220 · 1,210)
  — 주방 창 H58(↕)은 창 높이 580으로 봄
- 발코니 창 H130 · 98, 계량기 H157, 발코니 문 위 H2885(?)
  — 어느 치수인지 확인 · 문 양 끝 30 · 4도 확인
- 실측일 — 사진에 없음 (천장 높이는 모든 타입 2,300)

도면과 차이가 큰 곳

- 거실 아래 벽(발코니 문 끝 ~ 오른쪽 벽) 2,500 — 도면 2,765
  (발코니 가로 1,425와 맞지 않아 그리지 않음 · B1 실측 2,507도 같음)
- B-2형 샘플(분양 안내 그림의 치수 체인)보다 방이 작음 —
  침실2 2,720 × 3,220 → 2,370 × 2,880 · 거실 3,710 → 3,570
  B-2 실측은 B-1 실측(B1-real)과 거의 같은 크기